
GRUNDRISS / ARCHITEKTUR + TGA-POSITIONEN

Obergeschoss - Bürogebäude Lindenhof

Fiktives Gebäude | 24,00 × 16,00 m | 1:100 bei Druck auf A3 in 100 % | Nord oben

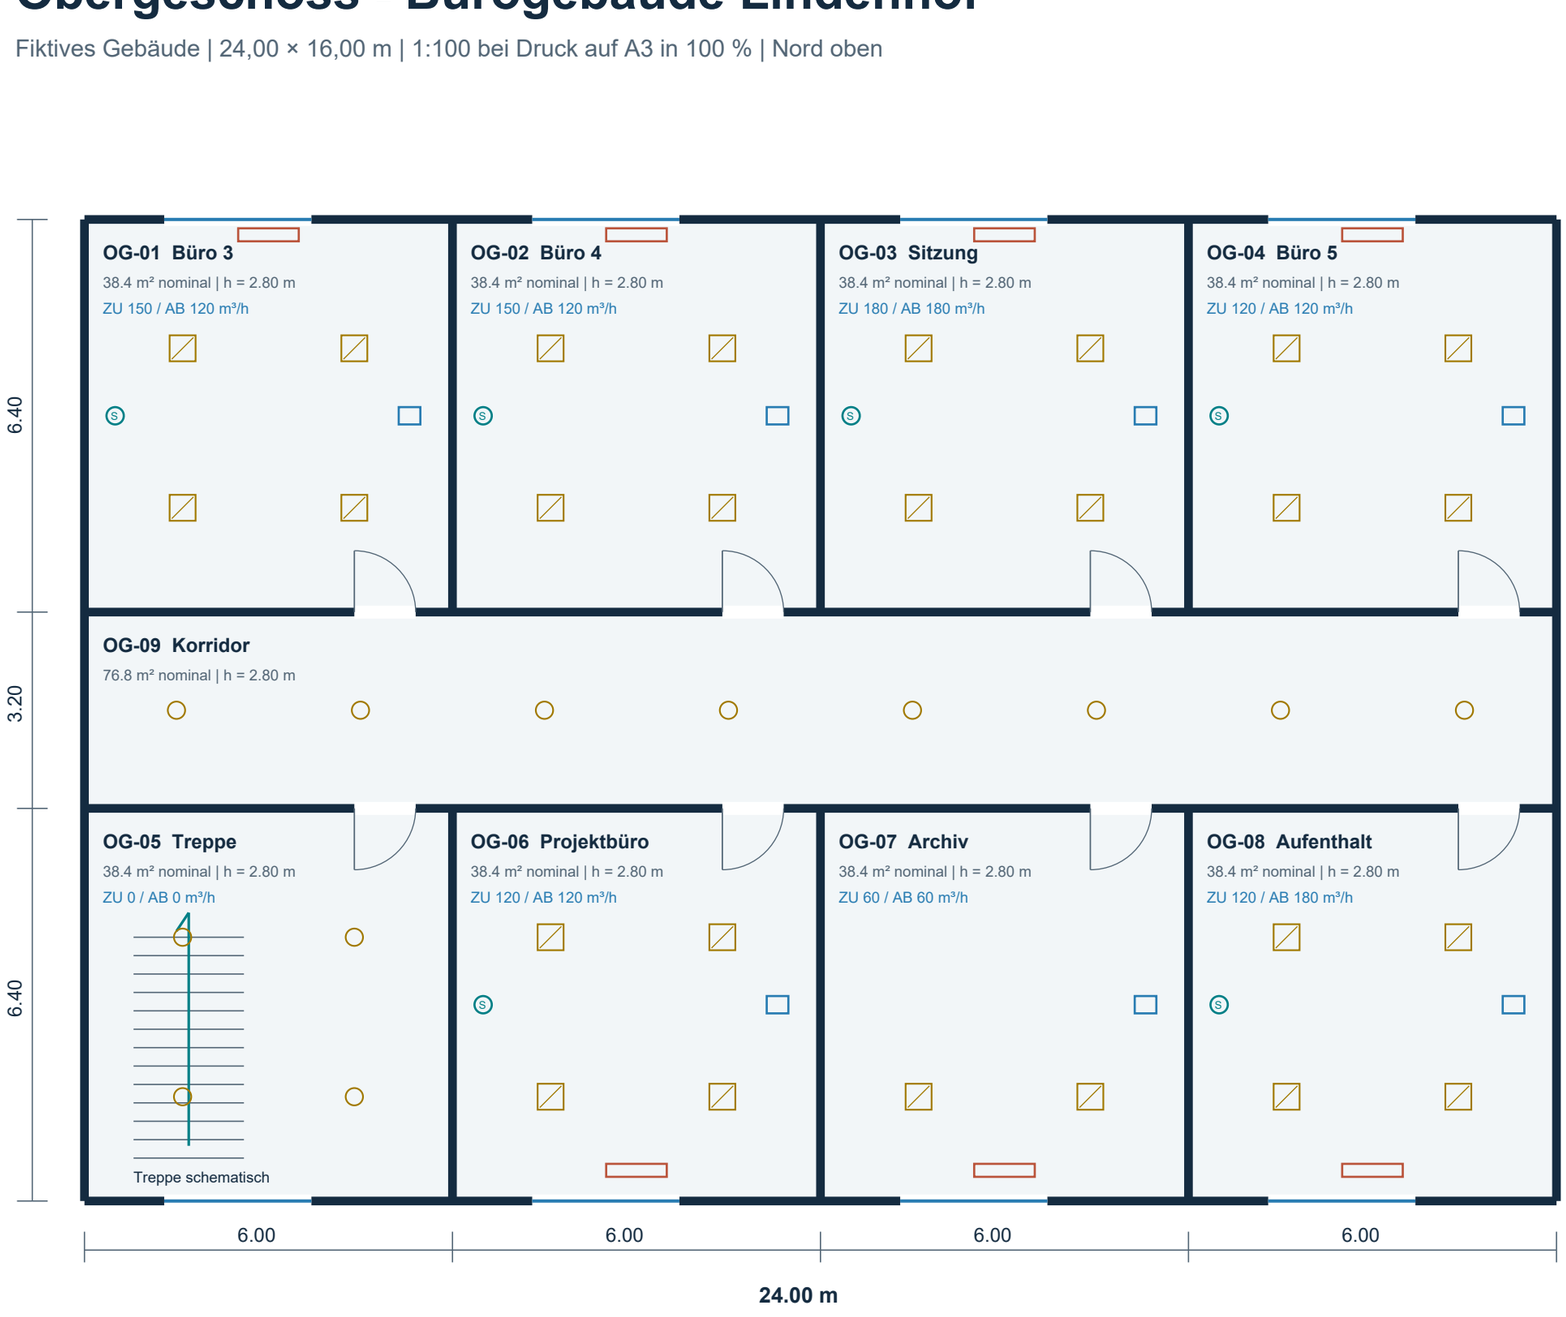

RAUM / AUSSTATTUNG

Typ-IDs verweisen auf die Datenblätter.

OG-01 Büro 3
4 × LT-01 | 1 × HK-01 | 1 × VAV-01
1 × CO2-01

OG-02 Büro 4
4 × LT-01 | 1 × HK-01 | 1 × VAV-01
1 × CO2-01

OG-03 Sitzung
4 × LT-01 | 1 × HK-01 | 1 × VAV-01
1 × CO2-01

OG-04 Büro 5
4 × LT-01 | 1 × HK-01 | 1 × VAV-01
1 × CO2-01

OG-05 Treppe
4 × LT-02

OG-06 Projektbüro
4 × LT-01 | 1 × HK-01 | 1 × VAV-01
1 × CO2-01

OG-07 Archiv
2 × LT-01 | 1 × HK-02 | 1 × VAV-01

OG-08 Aufenthalt
4 × LT-01 | 1 × HK-01 | 1 × VAV-01
1 × CO2-01

OG-09 Korridor
8 × LT-02

SYMBOLE / GRENZEN

Quadrat mit Diagonale: LT-01 / Kreis: LT-02
Roter Balken: HK / blaues Rechteck: VAV
Kreis S: CO2-01; MB und P direkt beschriftet
Positionen schematisch, Symbole nicht massstäblich
WP-01: Aussenaufstellung nördlich der Technik
Keine Leitungsführung oder Brandschutzplanung

MASSSTAB

0 — 5 m

Flächen aus Achsmassen; Wandstärken nicht abgezogen. Geschosshöhe 3,20 m.
Nutzungs-, Licht-, Wärme-, Luft- und Sicherheitsnachweise sind nicht Bestandteil.
TGA-Symbole und Türanschläge dienen ausschliesslich der Softwareprüfung.